

SR/A INTERIOR DESIGN
7020 WISCONSIN AVENUE
CHEVY CHASE MD 20815
301 560 3700
www.srainteriordesign.com

OWNER
MIDATLANTIC REALTY PARTNERS, LLC
3050 K St NW, Suite 125
Washington, DC 20007
202 719 9000

DESIGN ARCHITECT
SK+I ARCHITECTURAL DESIGN GROUP, LLC
4400 E West Hwy, Suite 700
Bethesda, MD 20814
301 454 9300

CIVIL ENGINEER
BOHLER DC
1331 Pennsylvania Ave NW,
Suite 1250 North
Washington, DC 20009
202 524 5700

STRUCTURAL ENGINEER
CARONO
1881 Campus Commons Dr,
Suite 103
Reston, VA 20191
703 391 0024

MEP
POWER DESIGN, INC
11600 Ninth St N
Saint Petersburg, FL 33716
727 210 0492

LANDSCAPE ARCHITECT
OCULUS
1611 Connecticut Ave NW
Washington, DC 20009
202 588 5454


WASHINGTON GATEWAY III

202 Florida Ave NE
Washington, DC 20002

© 2020 SR/A INTERIOR DESIGN
SR/A INTERIOR DESIGN EXPRESSLY RESERVES ITS
COMMON LAW COPYRIGHT AND OTHER
PROPRIETARY RIGHTS IN THIS DOCUMENT.
THESE DOCUMENTS ARE NOT TO BE
REPRODUCED, CHANGED, OR USED
FOR ANY PURPOSE OTHER THAN THE
PURPOSE FOR WHICH THEY WERE PROVIDED
OR CONSENT OF SR/A INTERIOR DESIGN.

SUBMISSION DATE
PROGRESS SET 12.24.19
95% CD SET 01.24.20
IFC SET 04.25.22

PROFESSIONAL SEAL

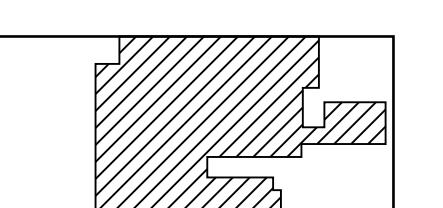

KEY
■ AREA OF WORK


© 2020 SR/A PROJECT NO.: 2019.366.00

FLOOR PLAN - LEVEL 1

CONSTRUCTION DOCUMENTATION

I-201

01


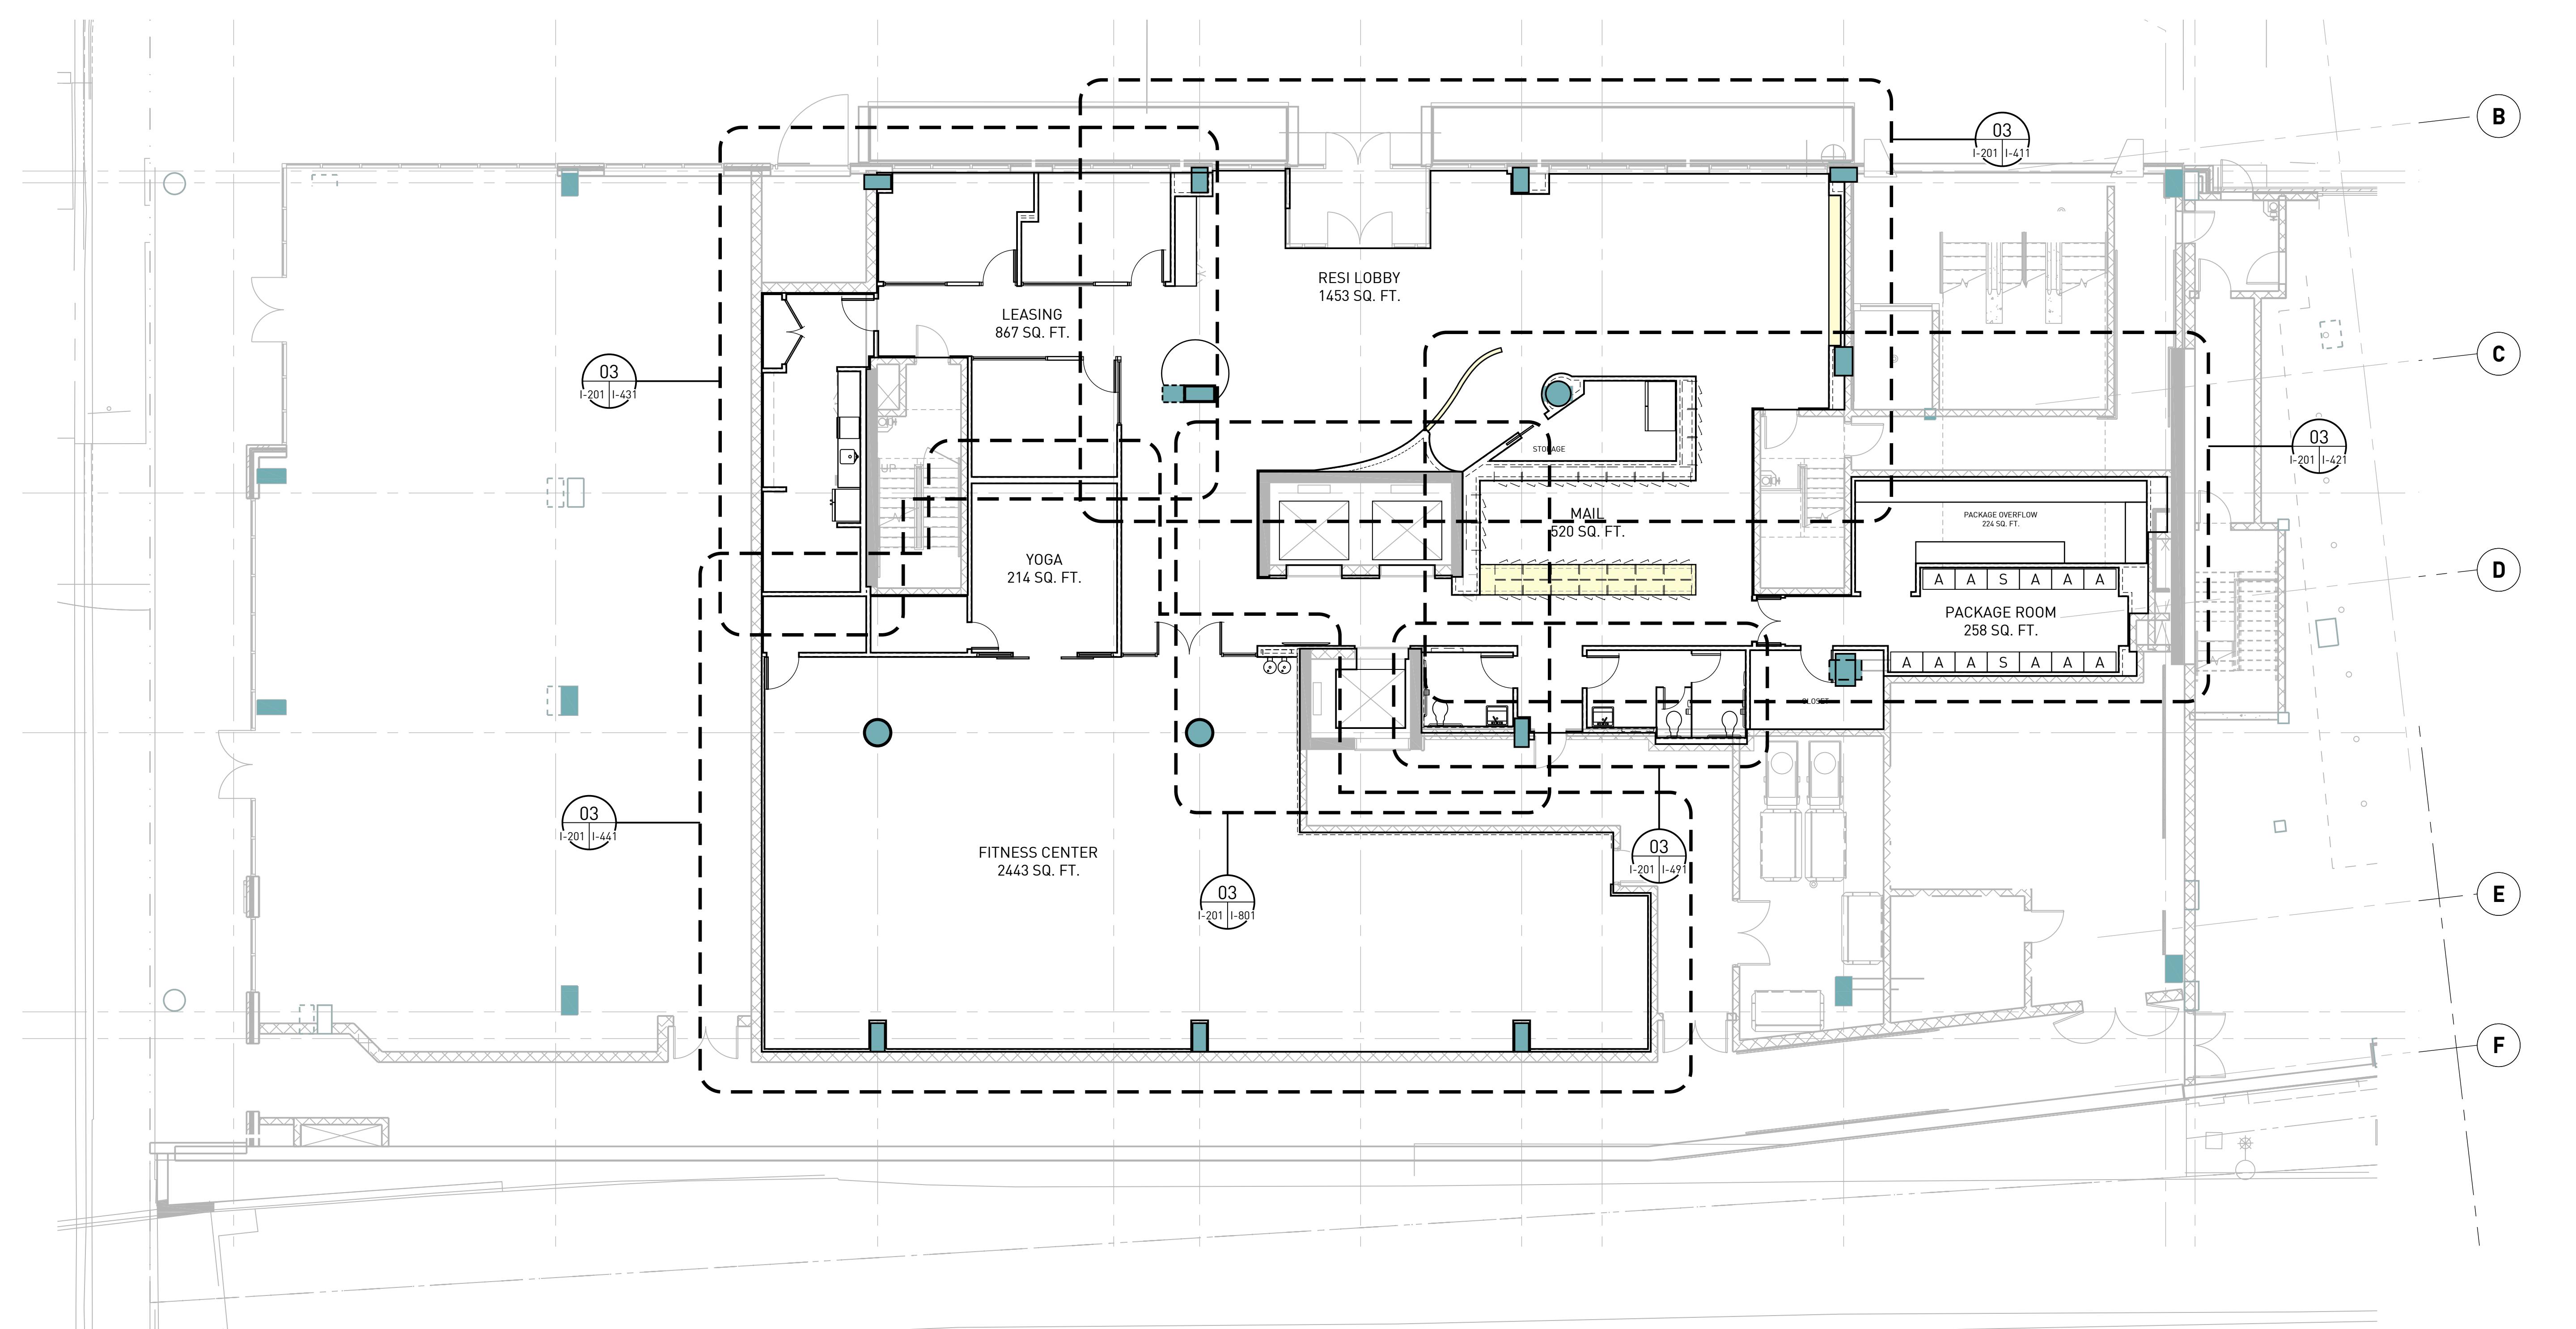


1/8" = 1'-0"


FLOOR PLAN - LEVEL 1

I-201

01

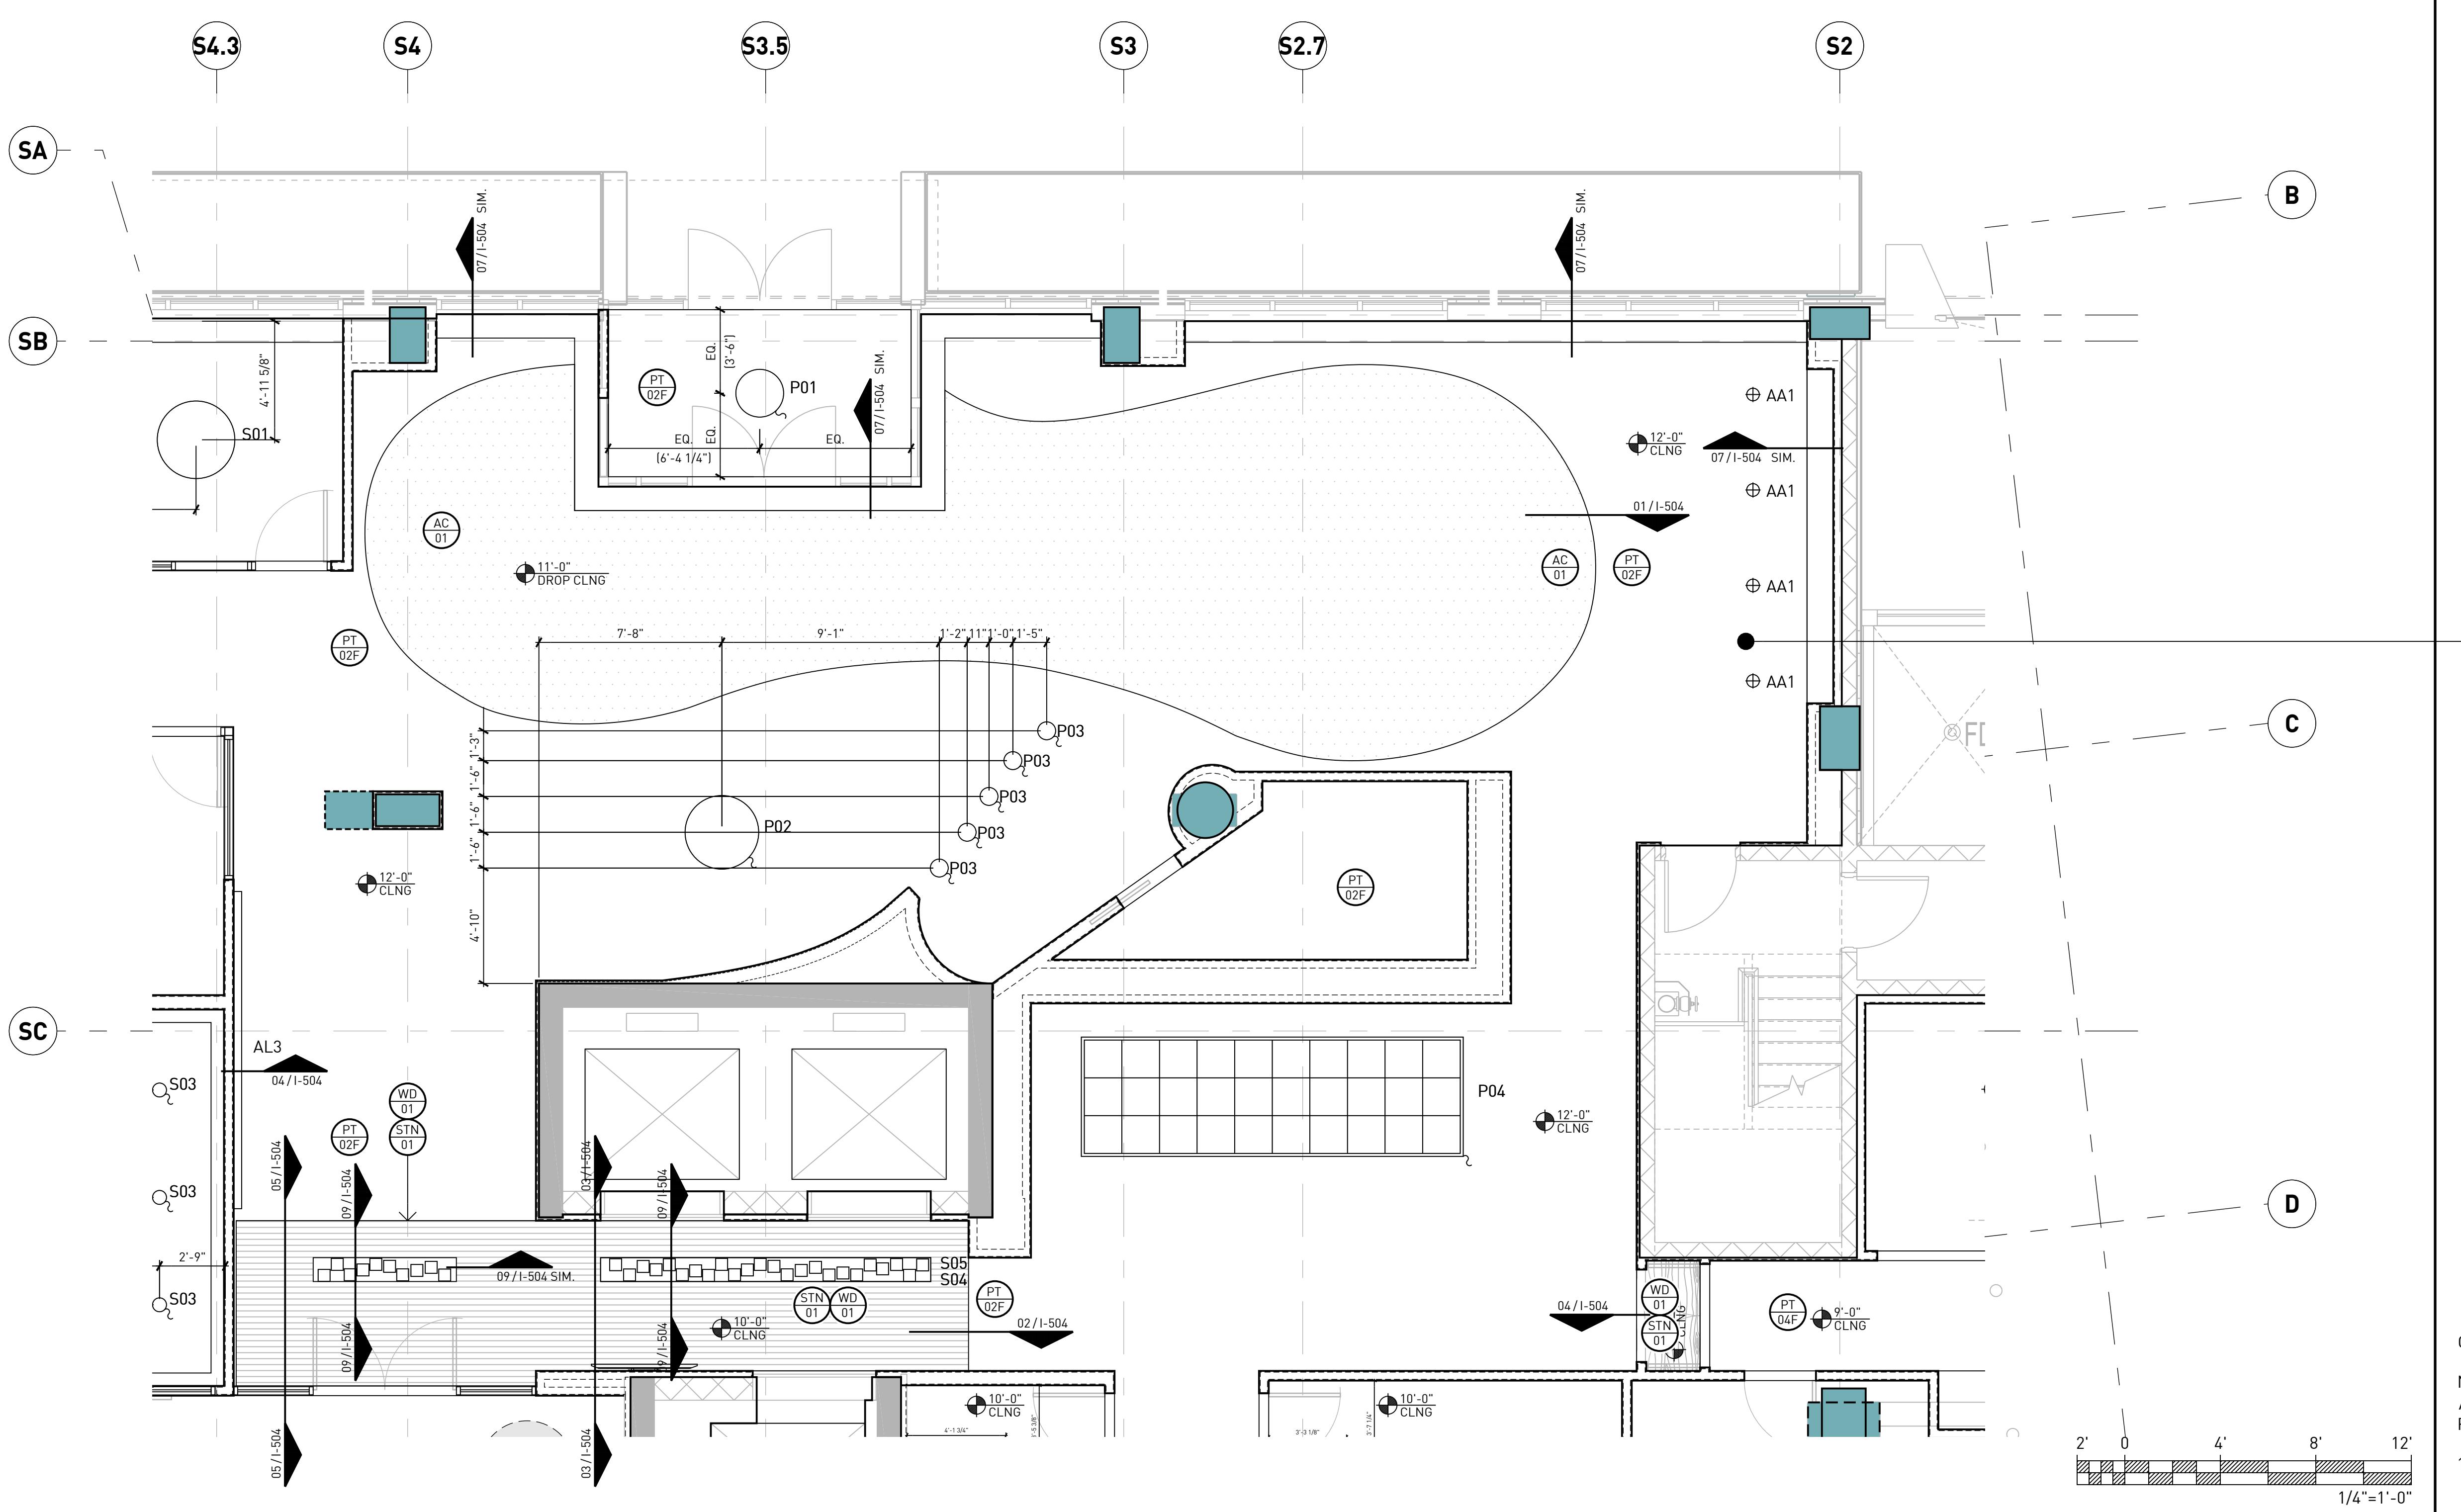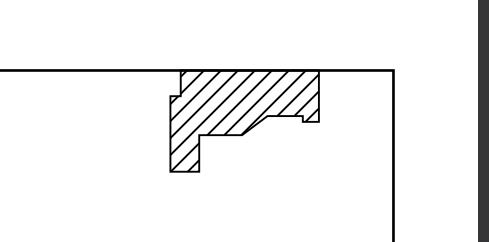

RESIDENTIAL LOBBY - REFLECTED CEILING PLAN 1/4"=1'-0" 04

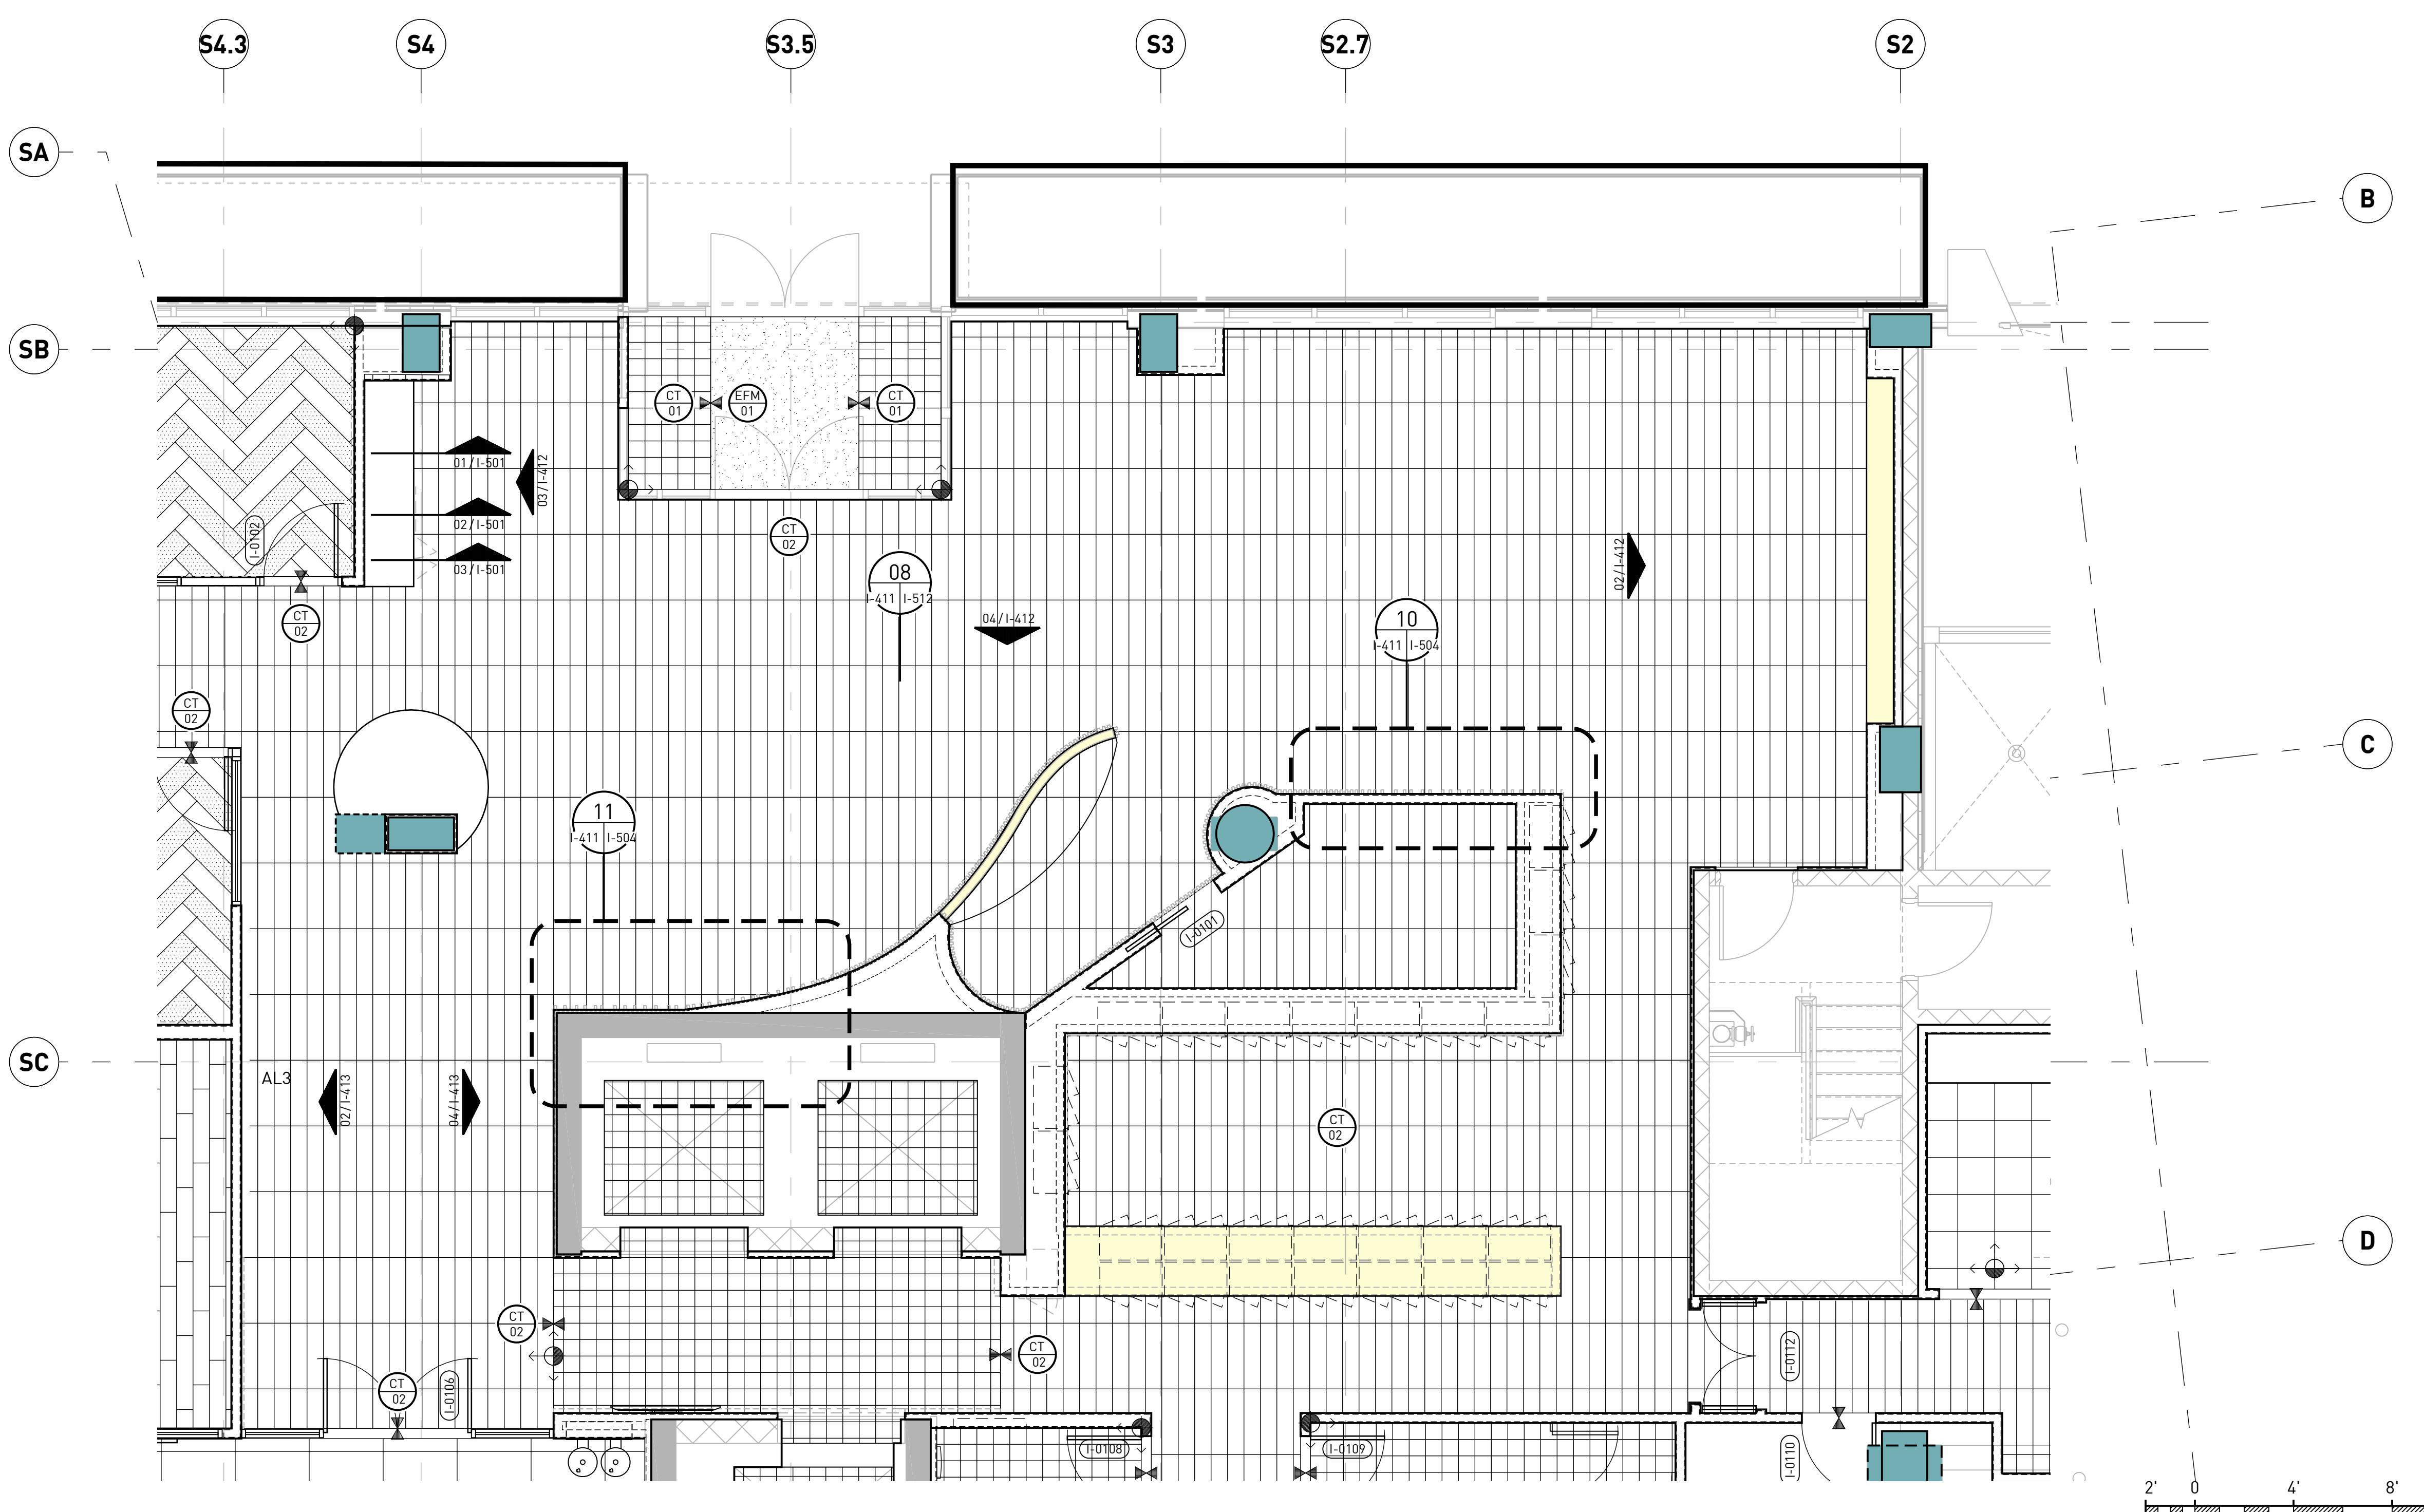

RESIDENTIAL LOBBY - FLOOR PLAN 1/4"=1'-0" 03

NOTES - CP NO SCALE L-XXX 02

NOTES - FP NO SCALE 01

